



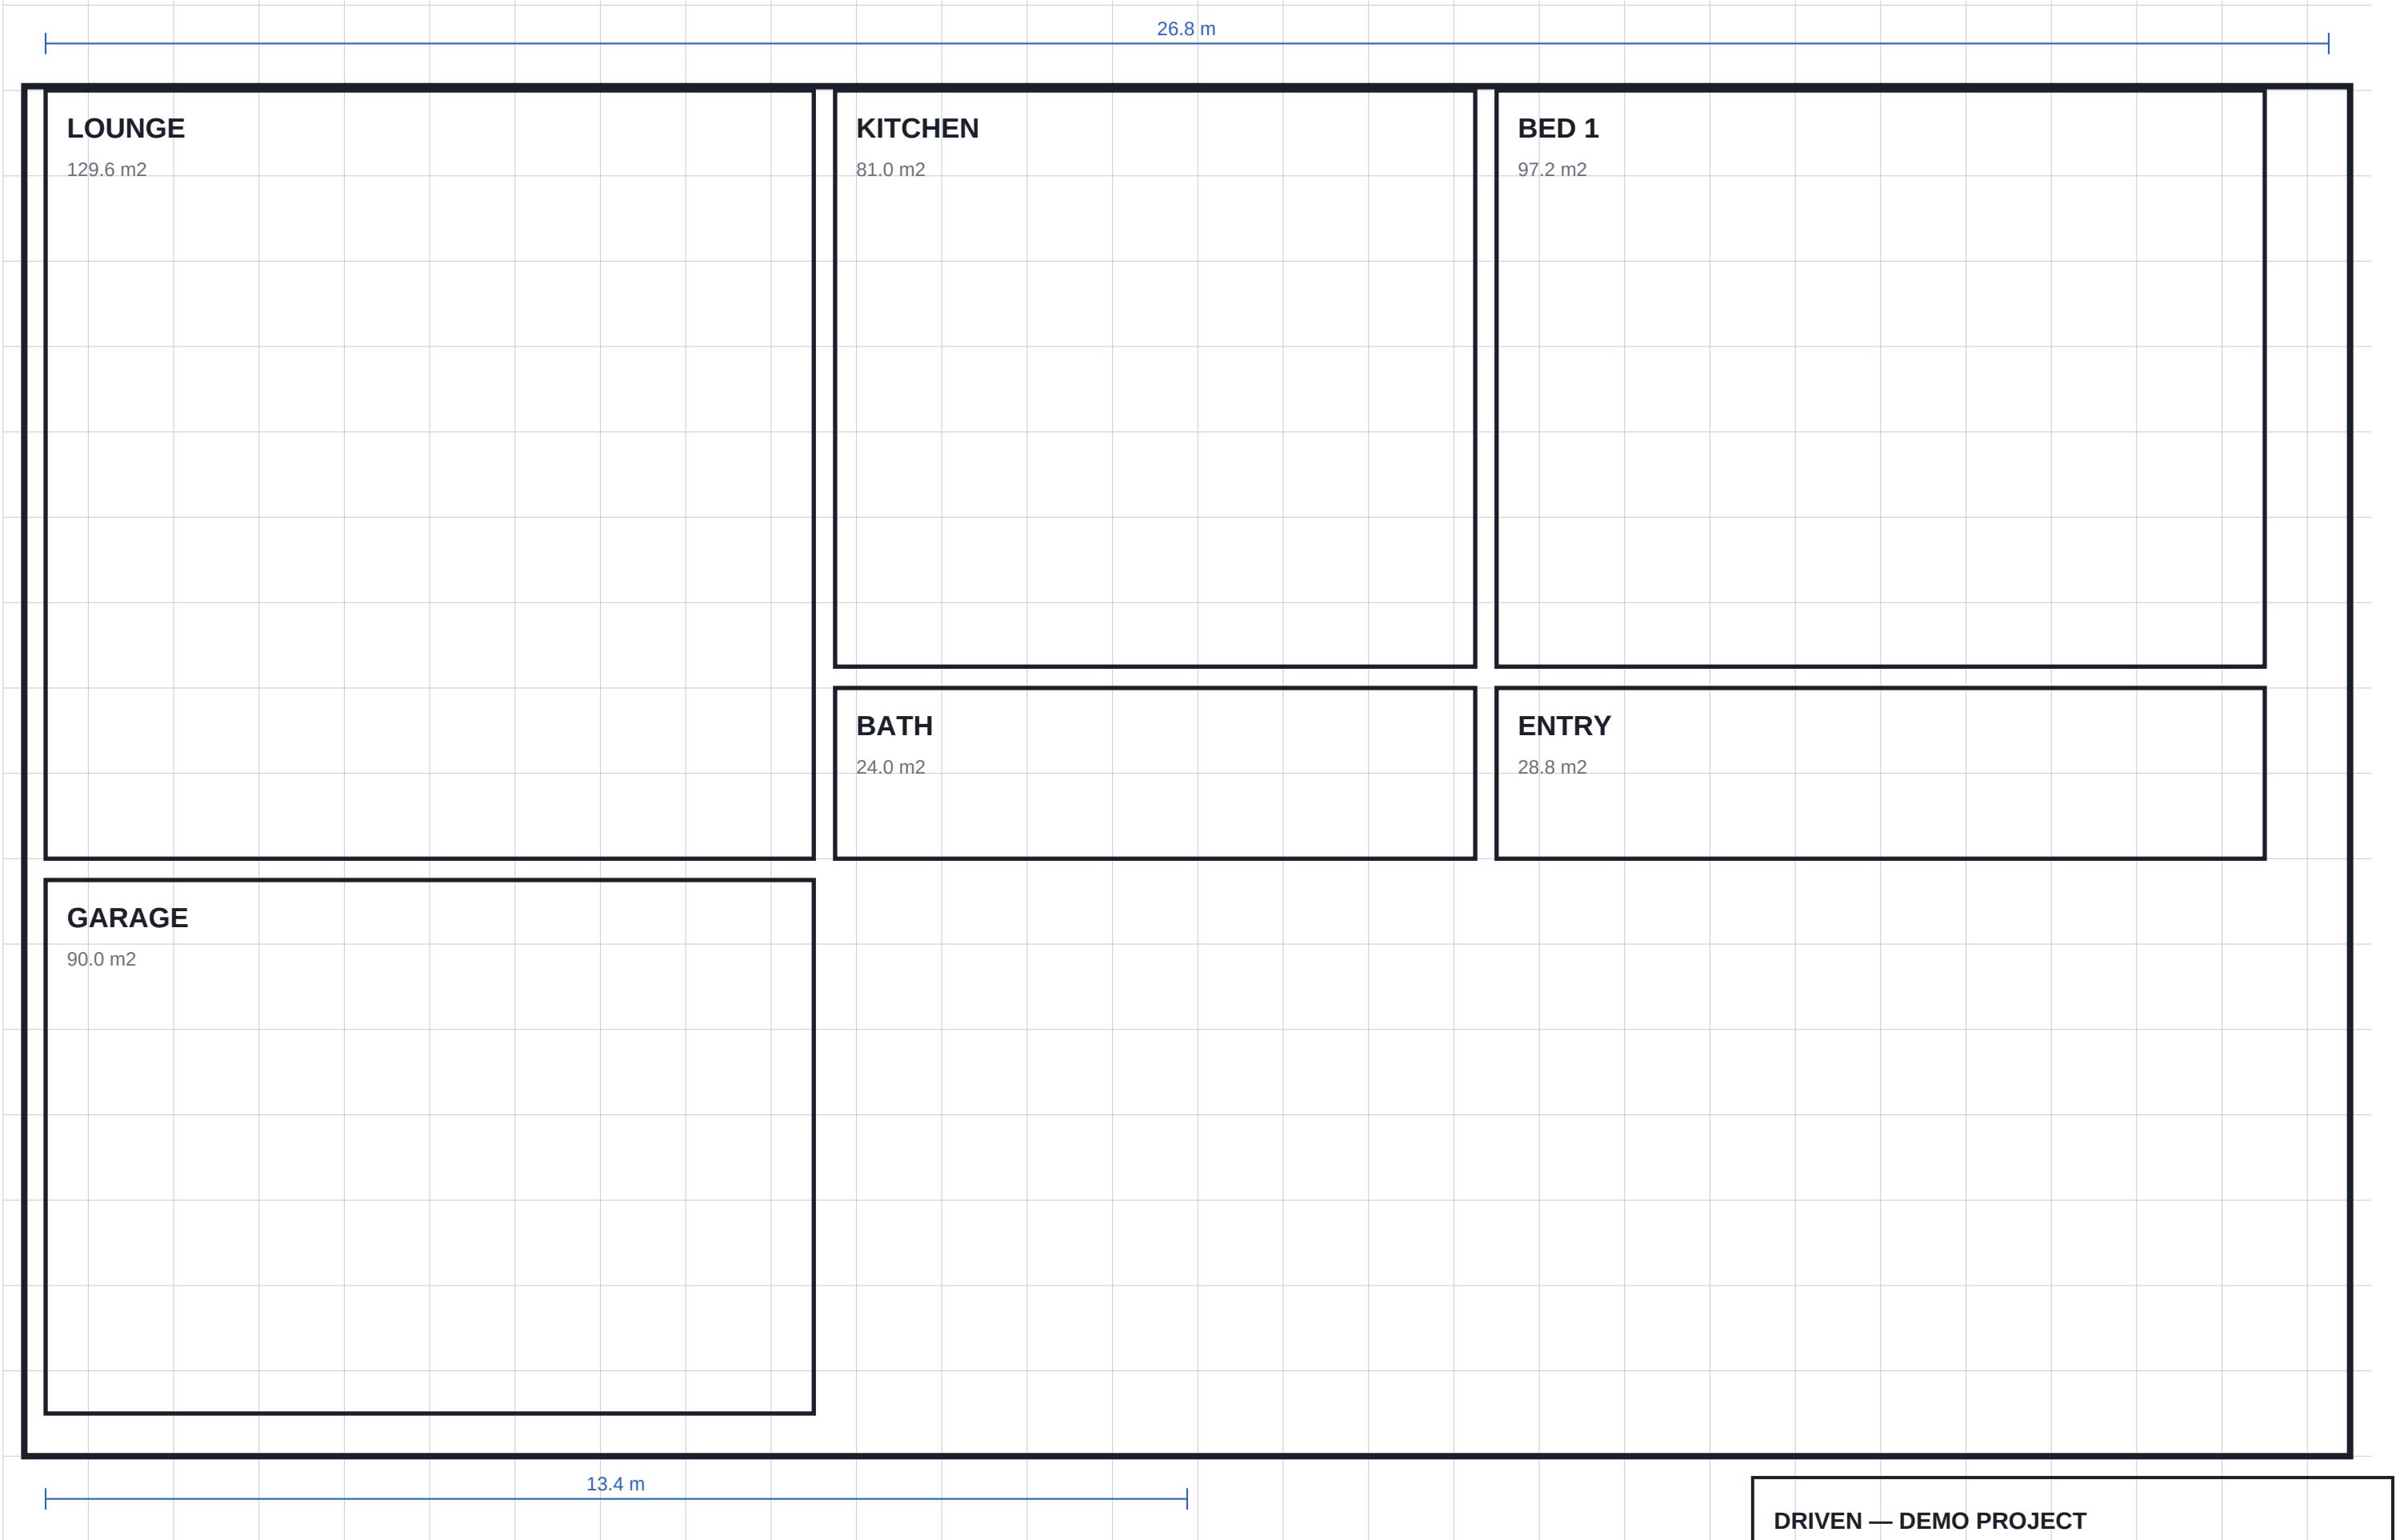


DRIVEN — DEMO PROJECT

GROUND FLOOR | SHEET A-01 of 5

SCALE 1:100 @ A3 NOT FOR CONSTRUCTION

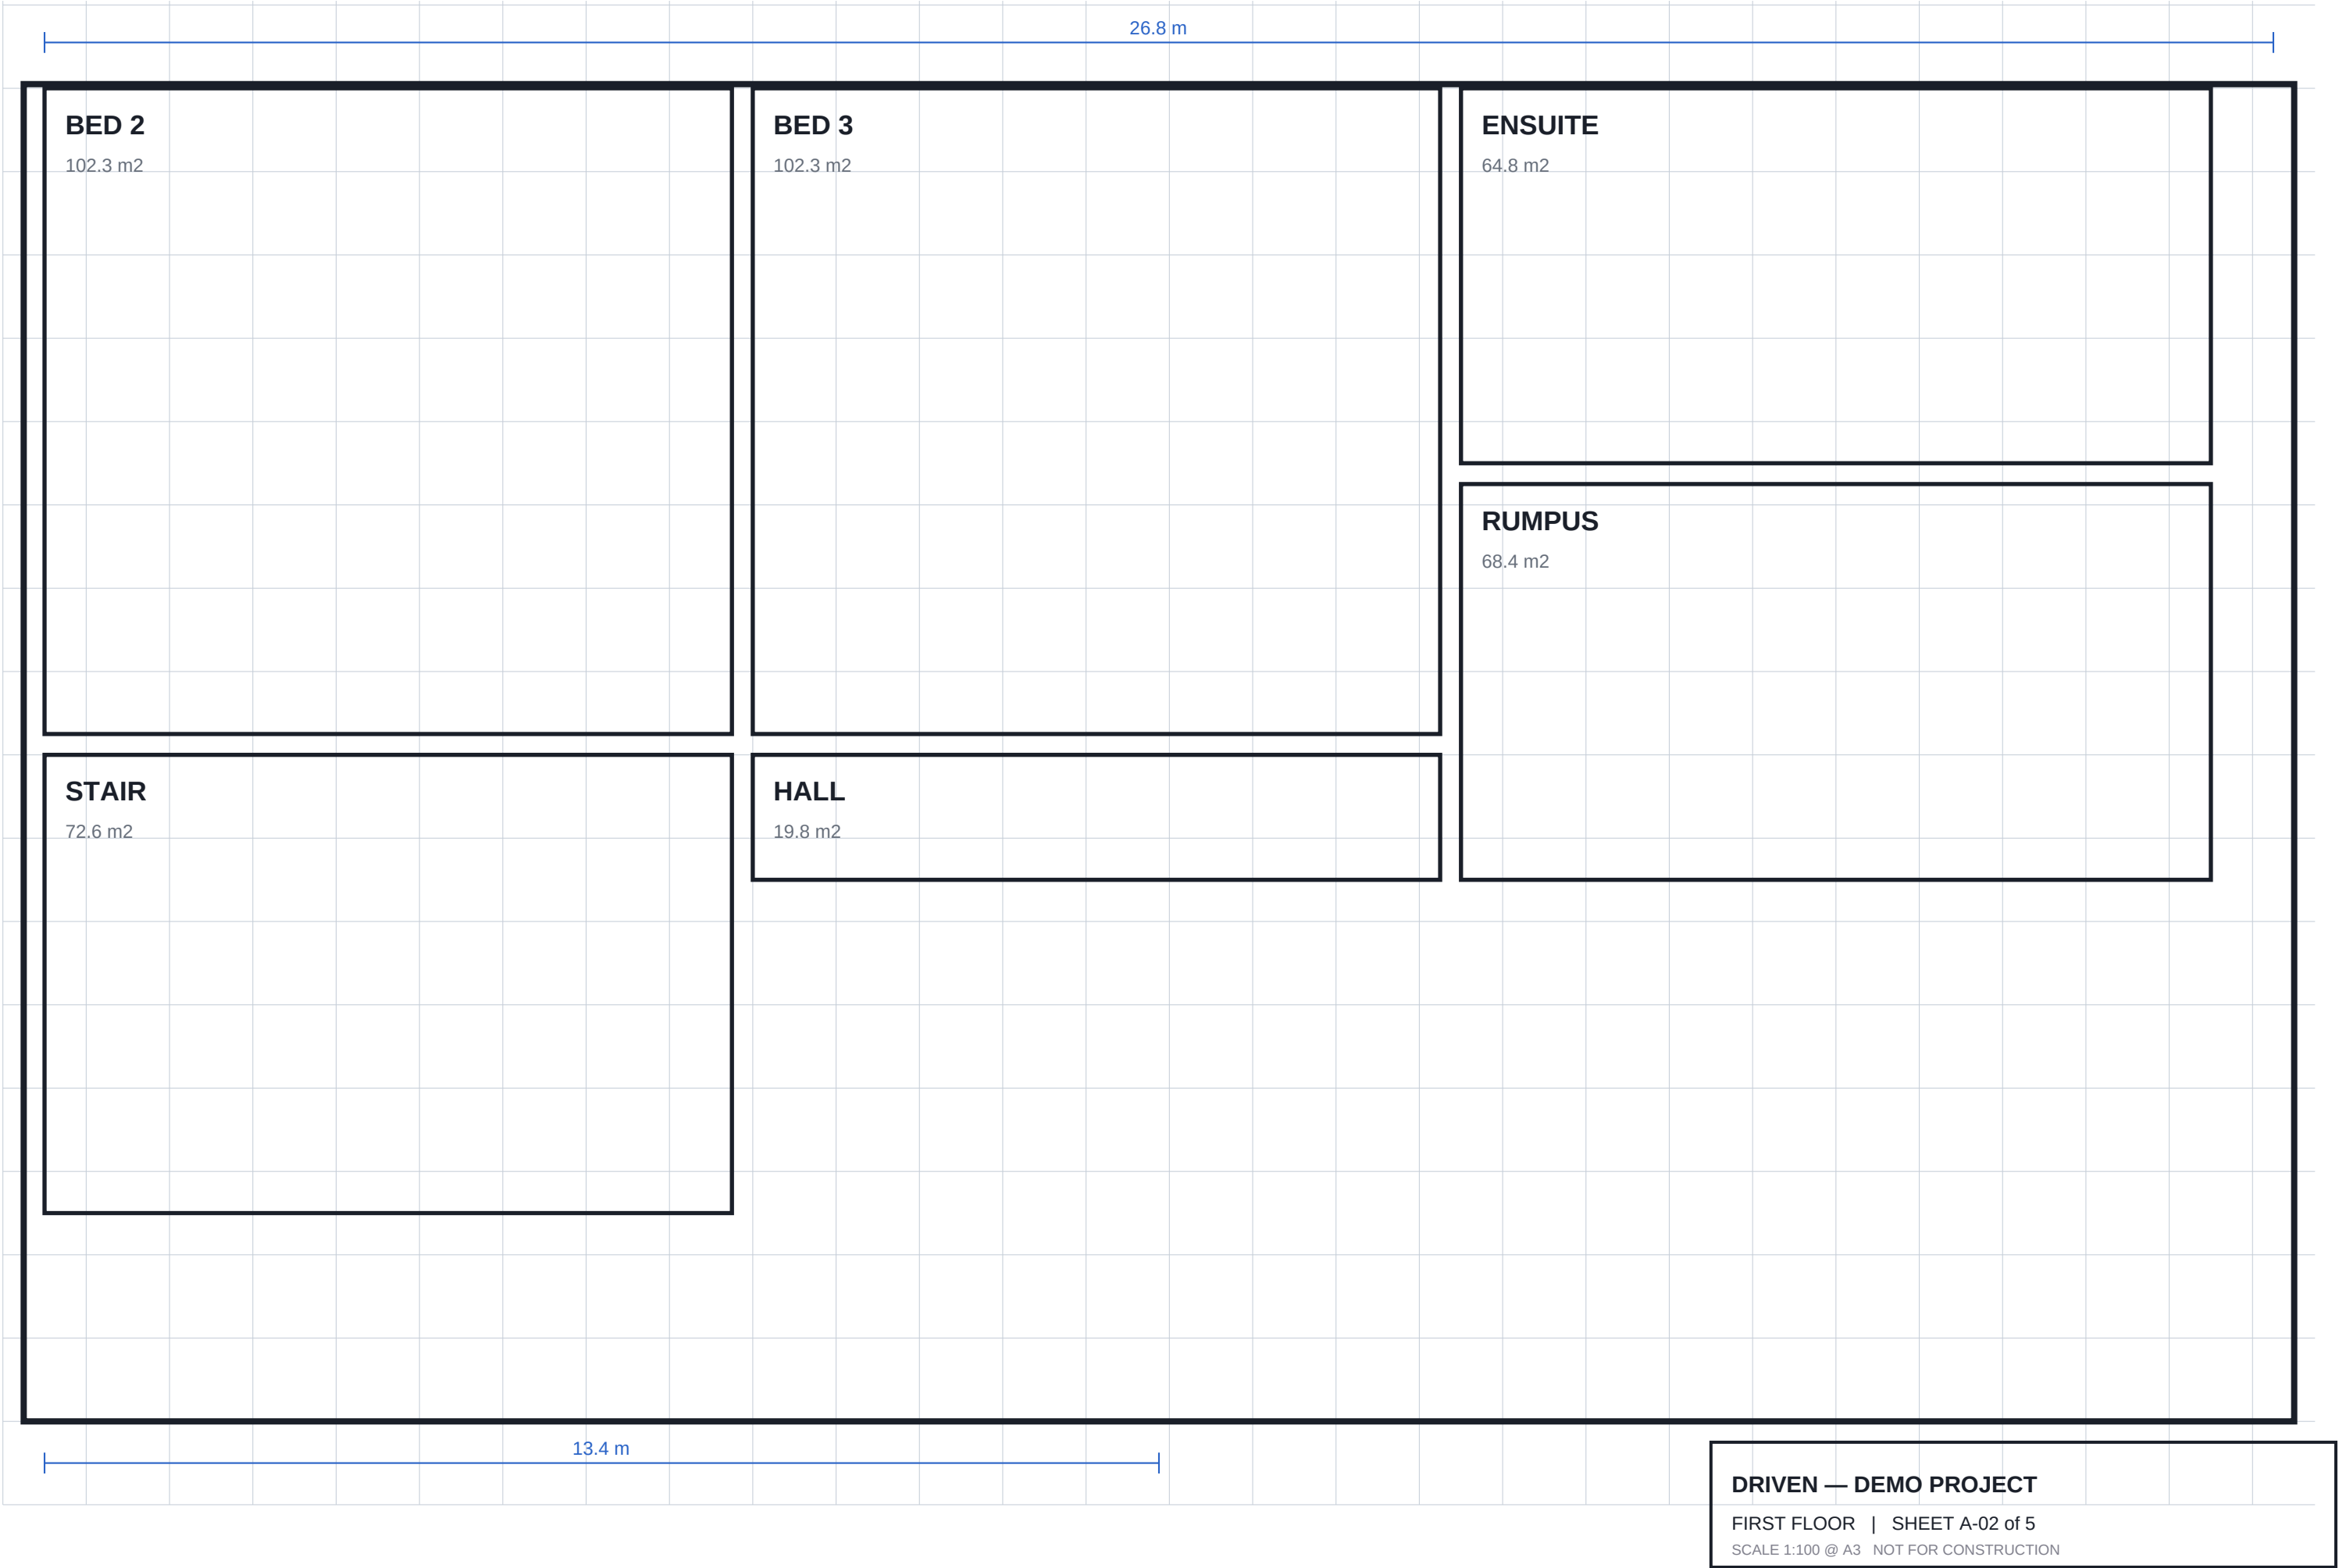



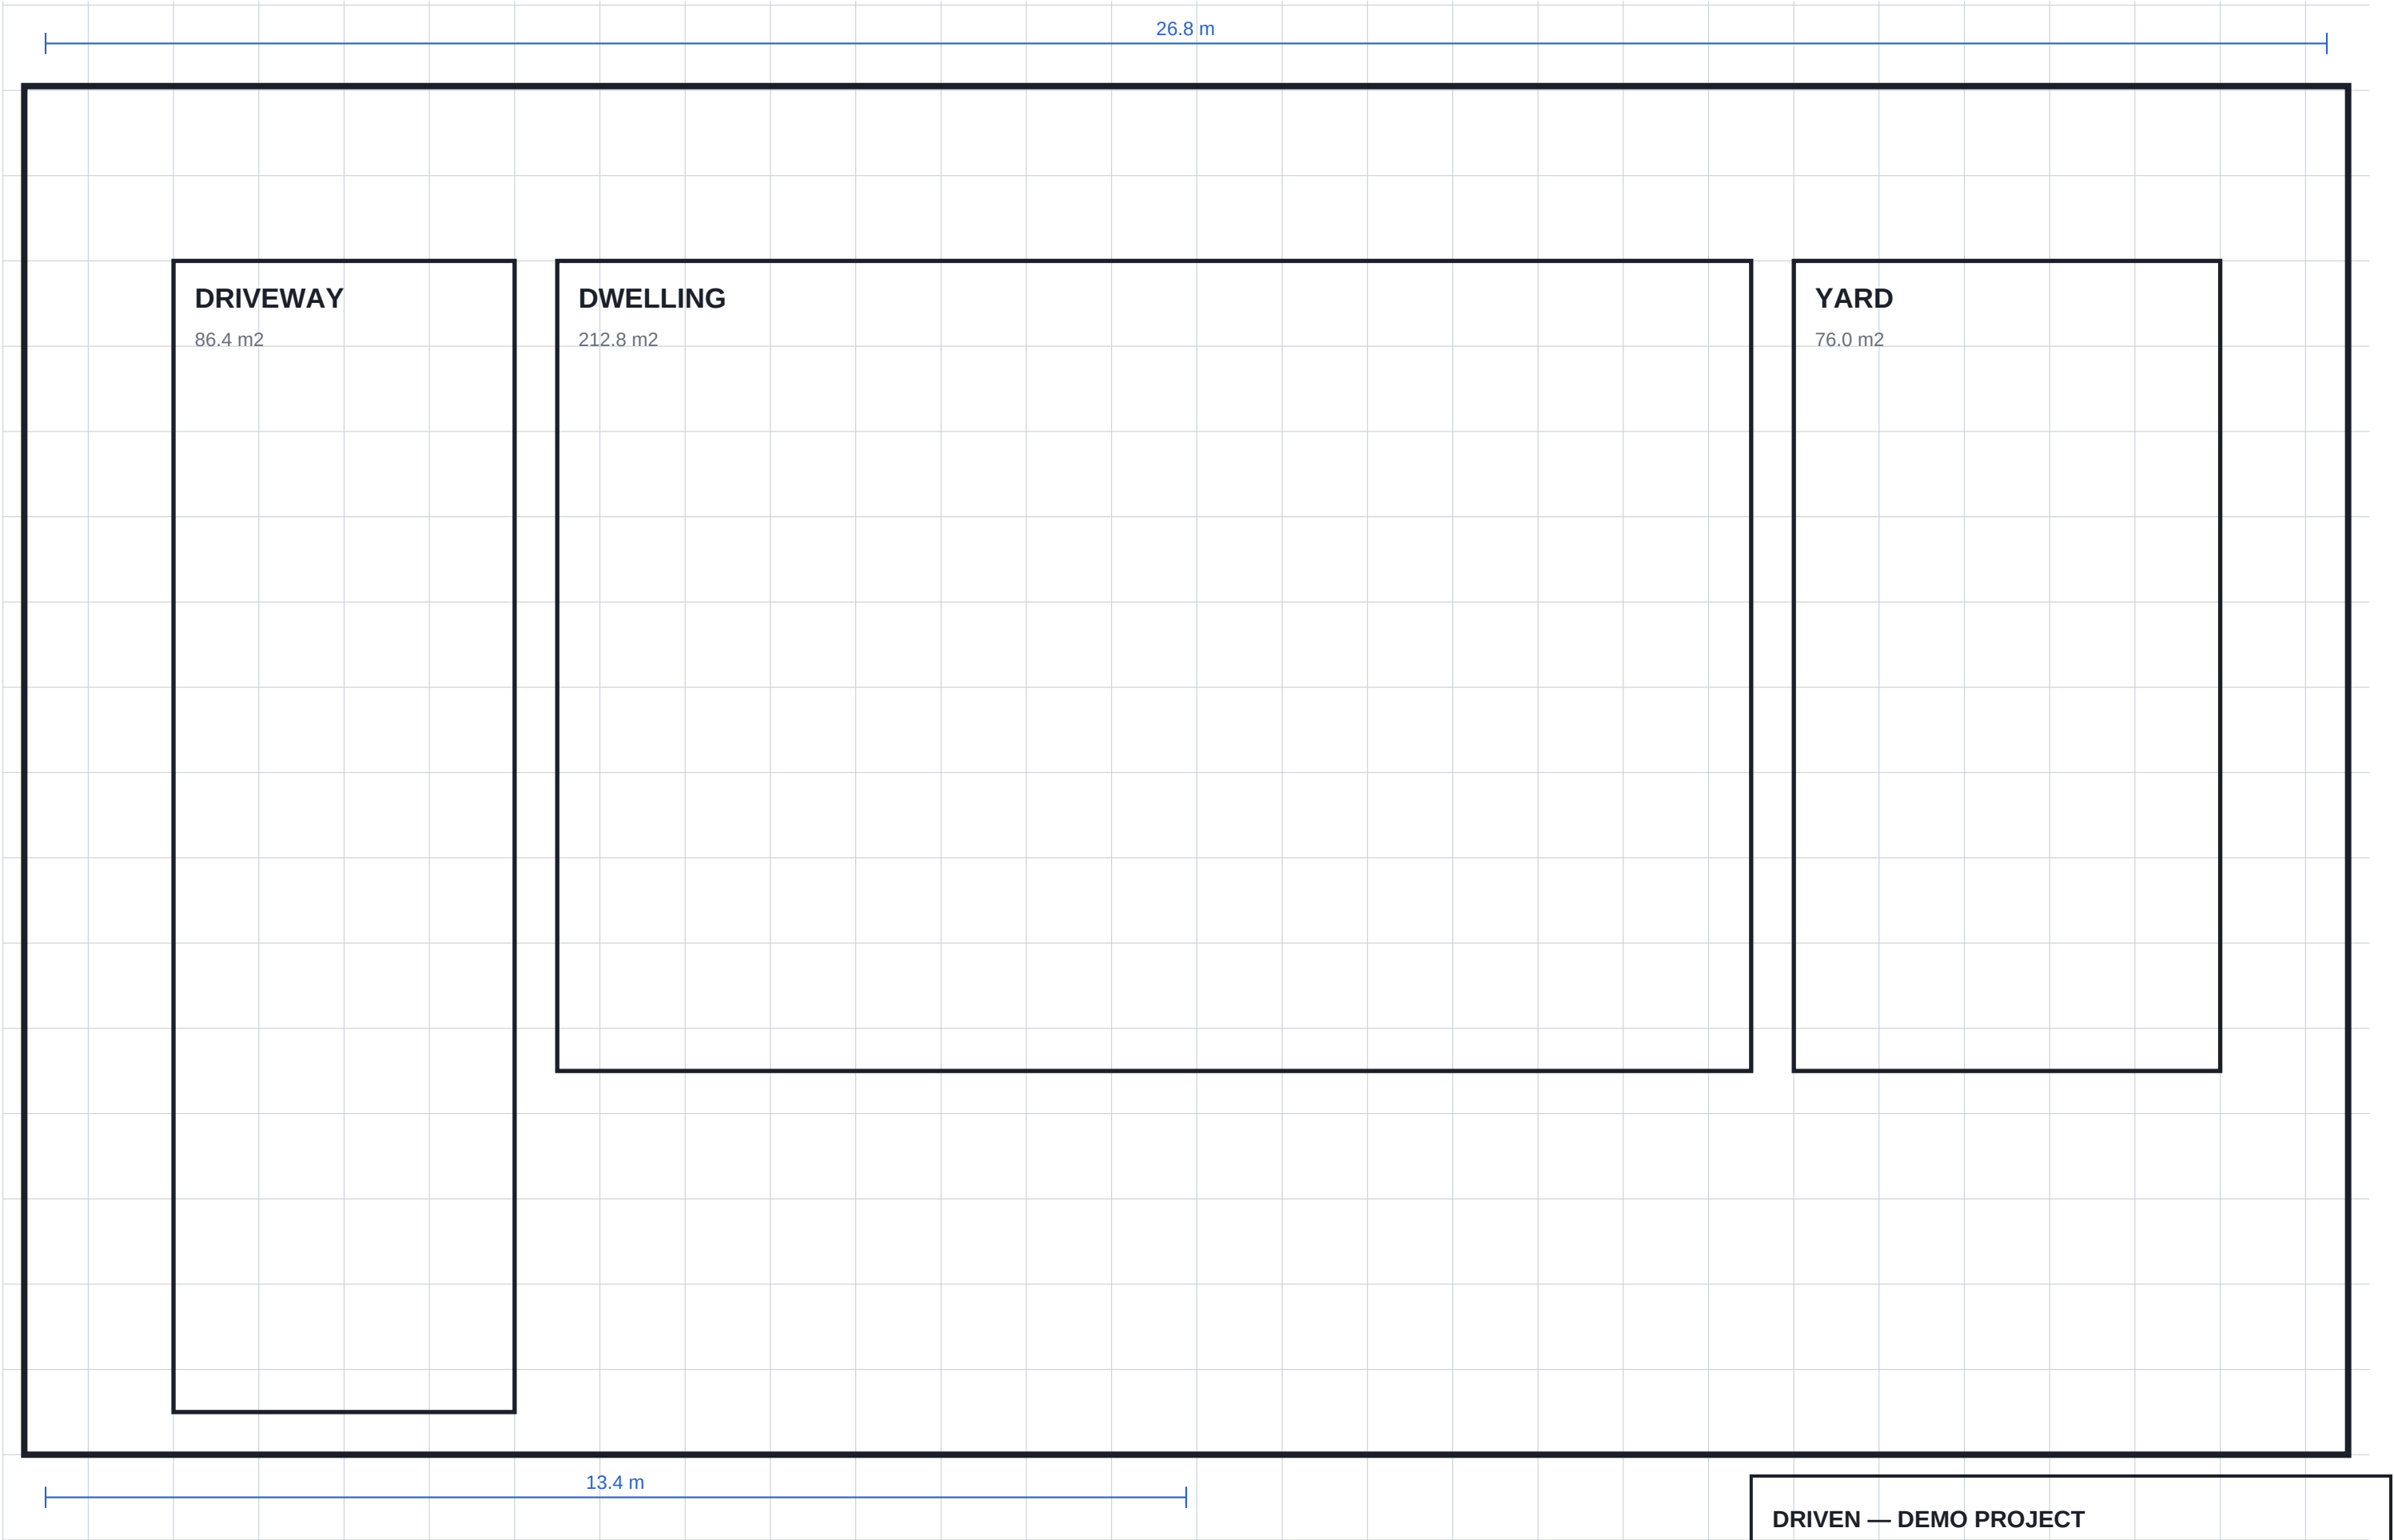

26.8 m

NORTH

115.2 m2

SOUTH

115.2 m2

EAST

115.2 m2

WEST

115.2 m2

13.4 m

DRIVEN — DEMO PROJECT

ELEVATIONS | SHEET A-05 of 5
SCALE 1:100 @ A3 NOT FOR CONSTRUCTION