


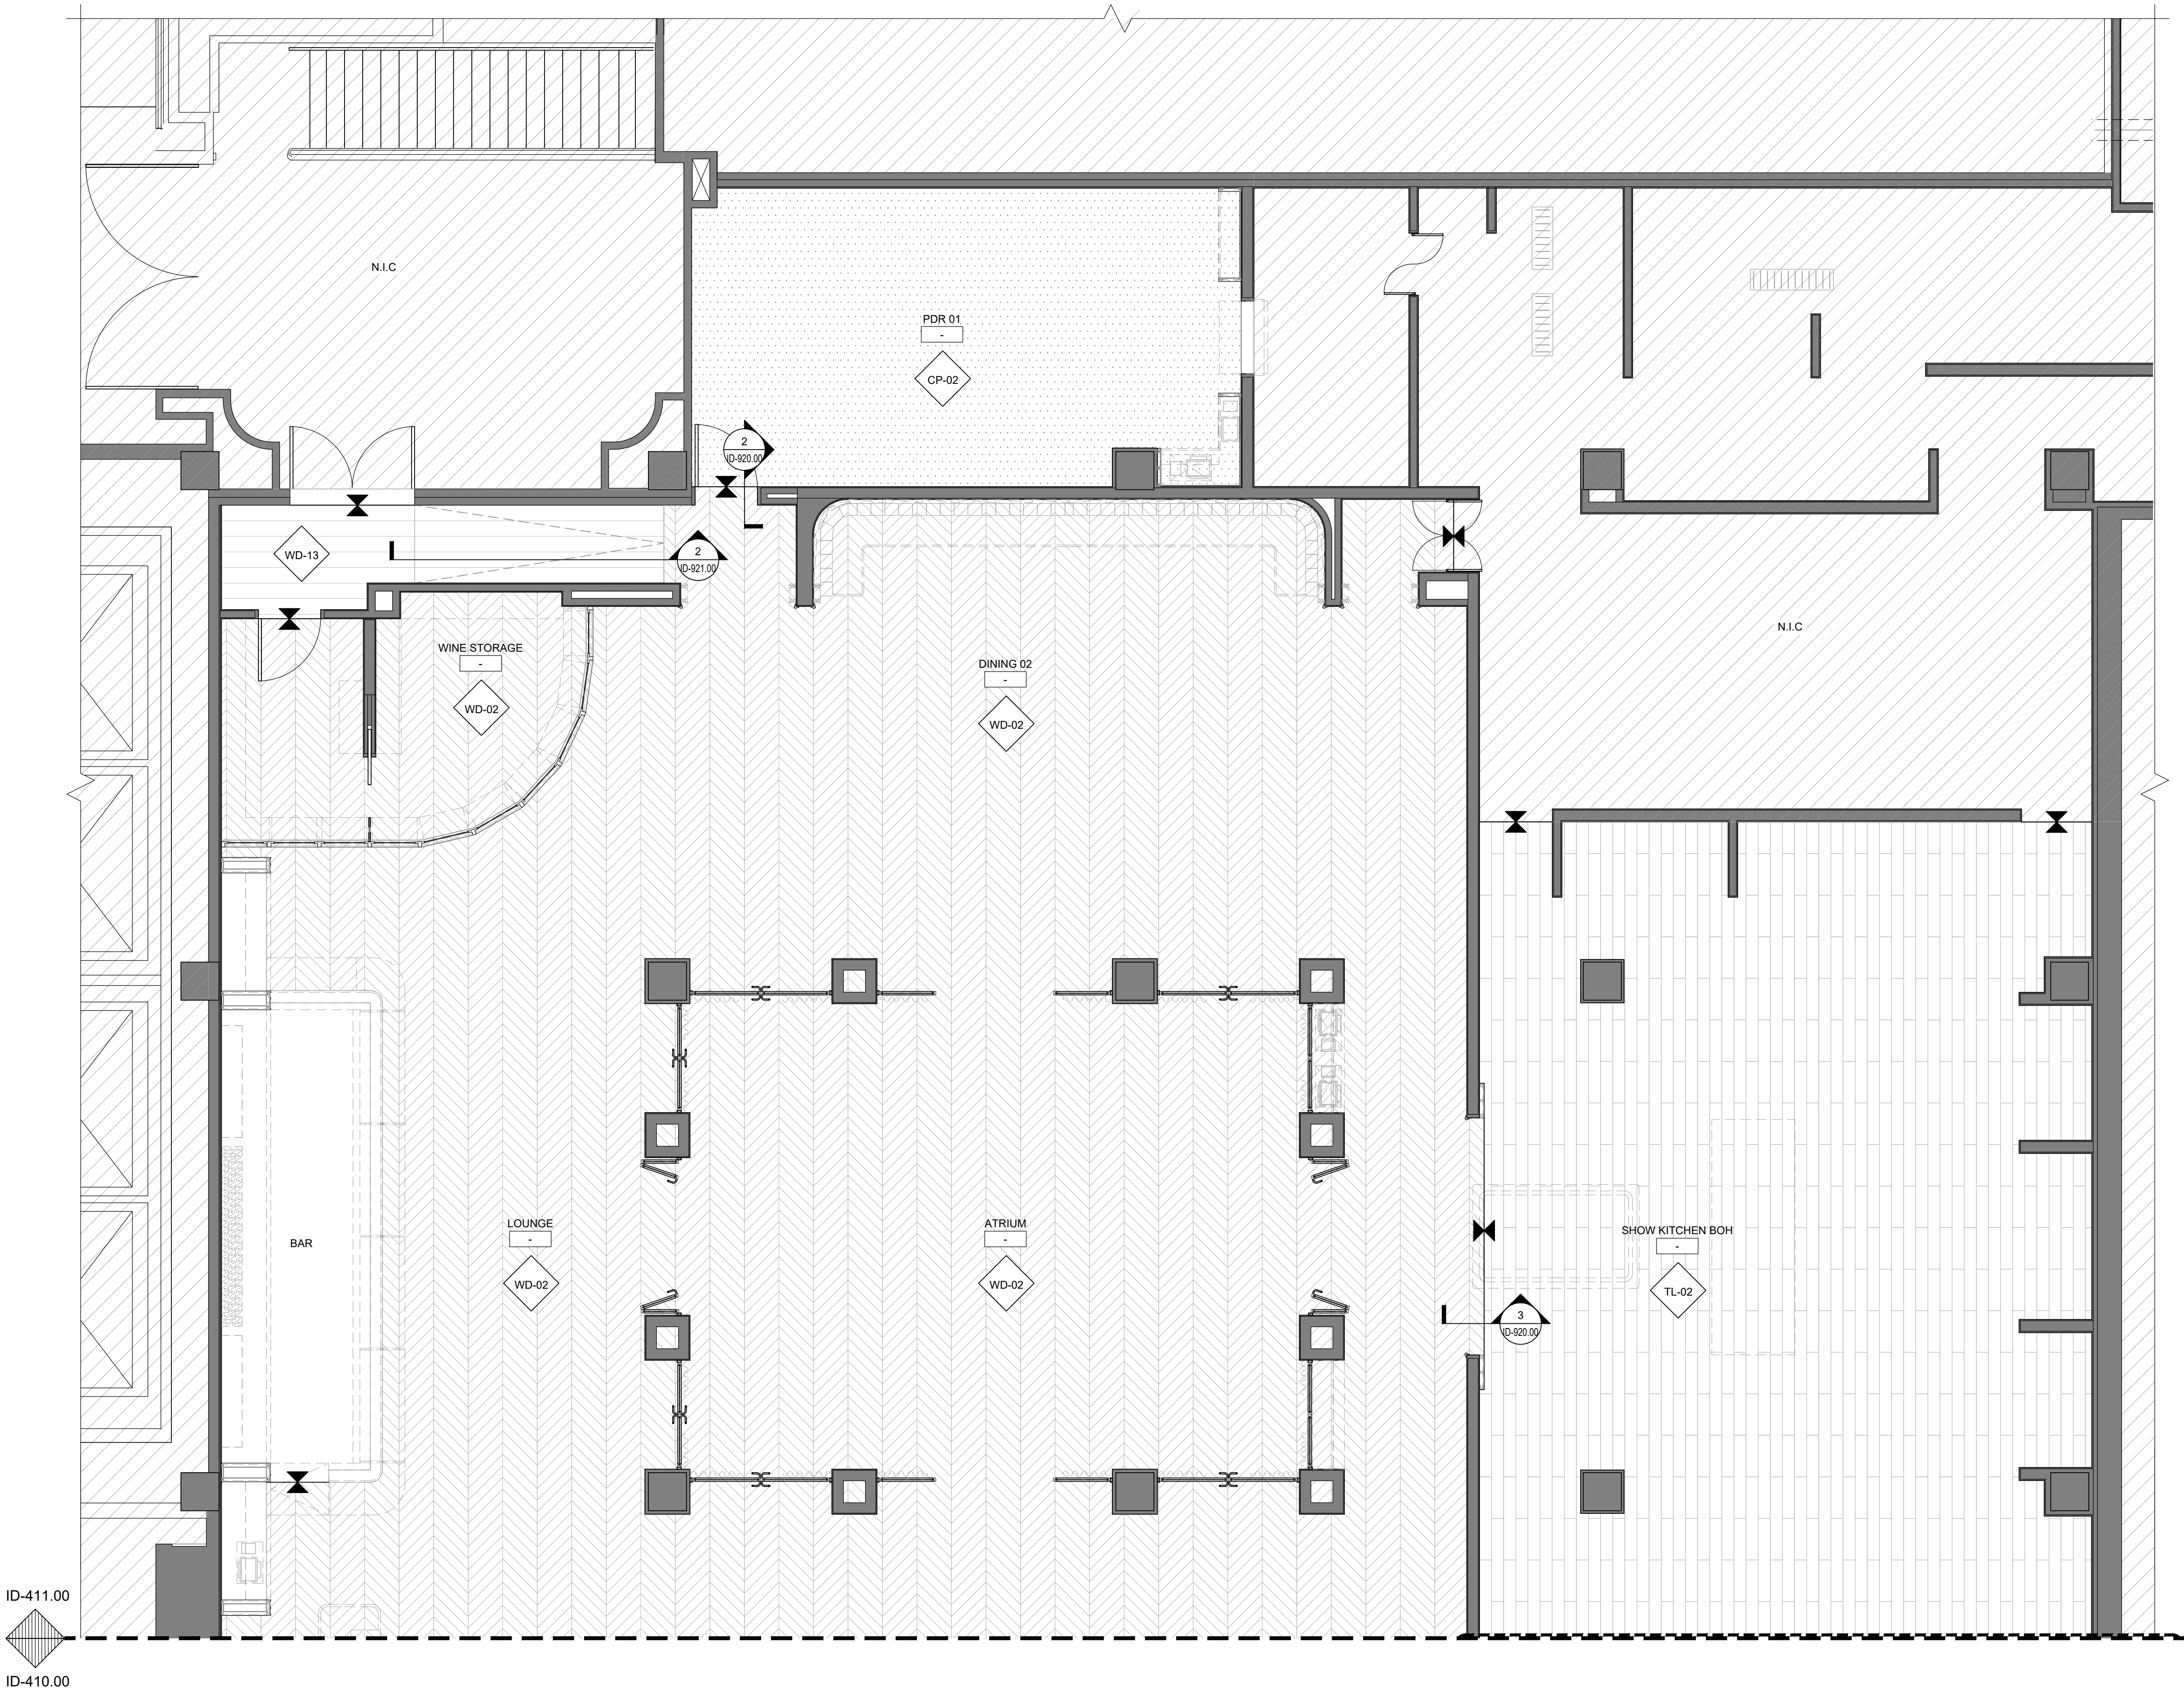

GENERAL NOTES

- A. SEE SHEET ID-1200.00 FOR FINISH SCHEDULE
- B. ALL FLOORING TO GO UNDER MILLWORK UNLESS OTHERWISE NOTED.
- C. ALL FLOORING TRANSITIONS TO BE FLUSH UNLESS OTHERWISE NOTED.
- D. MOCK UP OF TILE INSTALLATION WITH GROUT LINES TO BE REVIEWED AND APPROVED BY STUDIO K PRIOR TO COMPLETION OF INSTALL.

KEY NOTES

1. XXX

FLOOR SYMBOL LEGEND

- TILE STARTING TAG
- XX-XX
- FLOOR FINISH TRANSITION TAG

CASS CALDER SMITH

ARCHITECTURE
INTERIORS

180 VARICK ST. #830
NEW YORK, NY 10014
212.274.1121
CASSCALDERSMITH.COM

OWNER
MAPLE HOSPITALITY GROUP

ARCHITECT
CCS ARCHITECTURE

STRUCTURAL
WRG ENGINEERING

FIRE PROTECTION & MEP
MG ENGINEERING D.P.C.

INTERIOR DESIGN
STUDIO K CREATIVE

FOOD SERVICE
GREAT LAKES CULINARY
DESIGNS

LIGHTING DESIGN
CARROLL CONSULTING

AVIT/SECURITY
GLOBAL AV GROUP

PROJECT NAME

**MAPLE & ASH
NEW YORK, NY**

NORTH

SOUTH

ISSUED	DESCRIPTION
10/01/2025	ISSUE FOR 50% PROGRESS SET
10/14/2025	ALT 2
10/31/2025	ISSUE FOR 100% PROGRESS SET
11/12/2025	ALT 2

SHEET TITLE

**FLOOR FINISH
PLAN**

FILE
BY STUDIO K
SCALE AS NOTED
SHEET


ID-411.00

1 FLOOR FINISH PLAN
RESTAURANT

Scale: 1/4" = 1'-0"


ID-511.00

ID-510.00

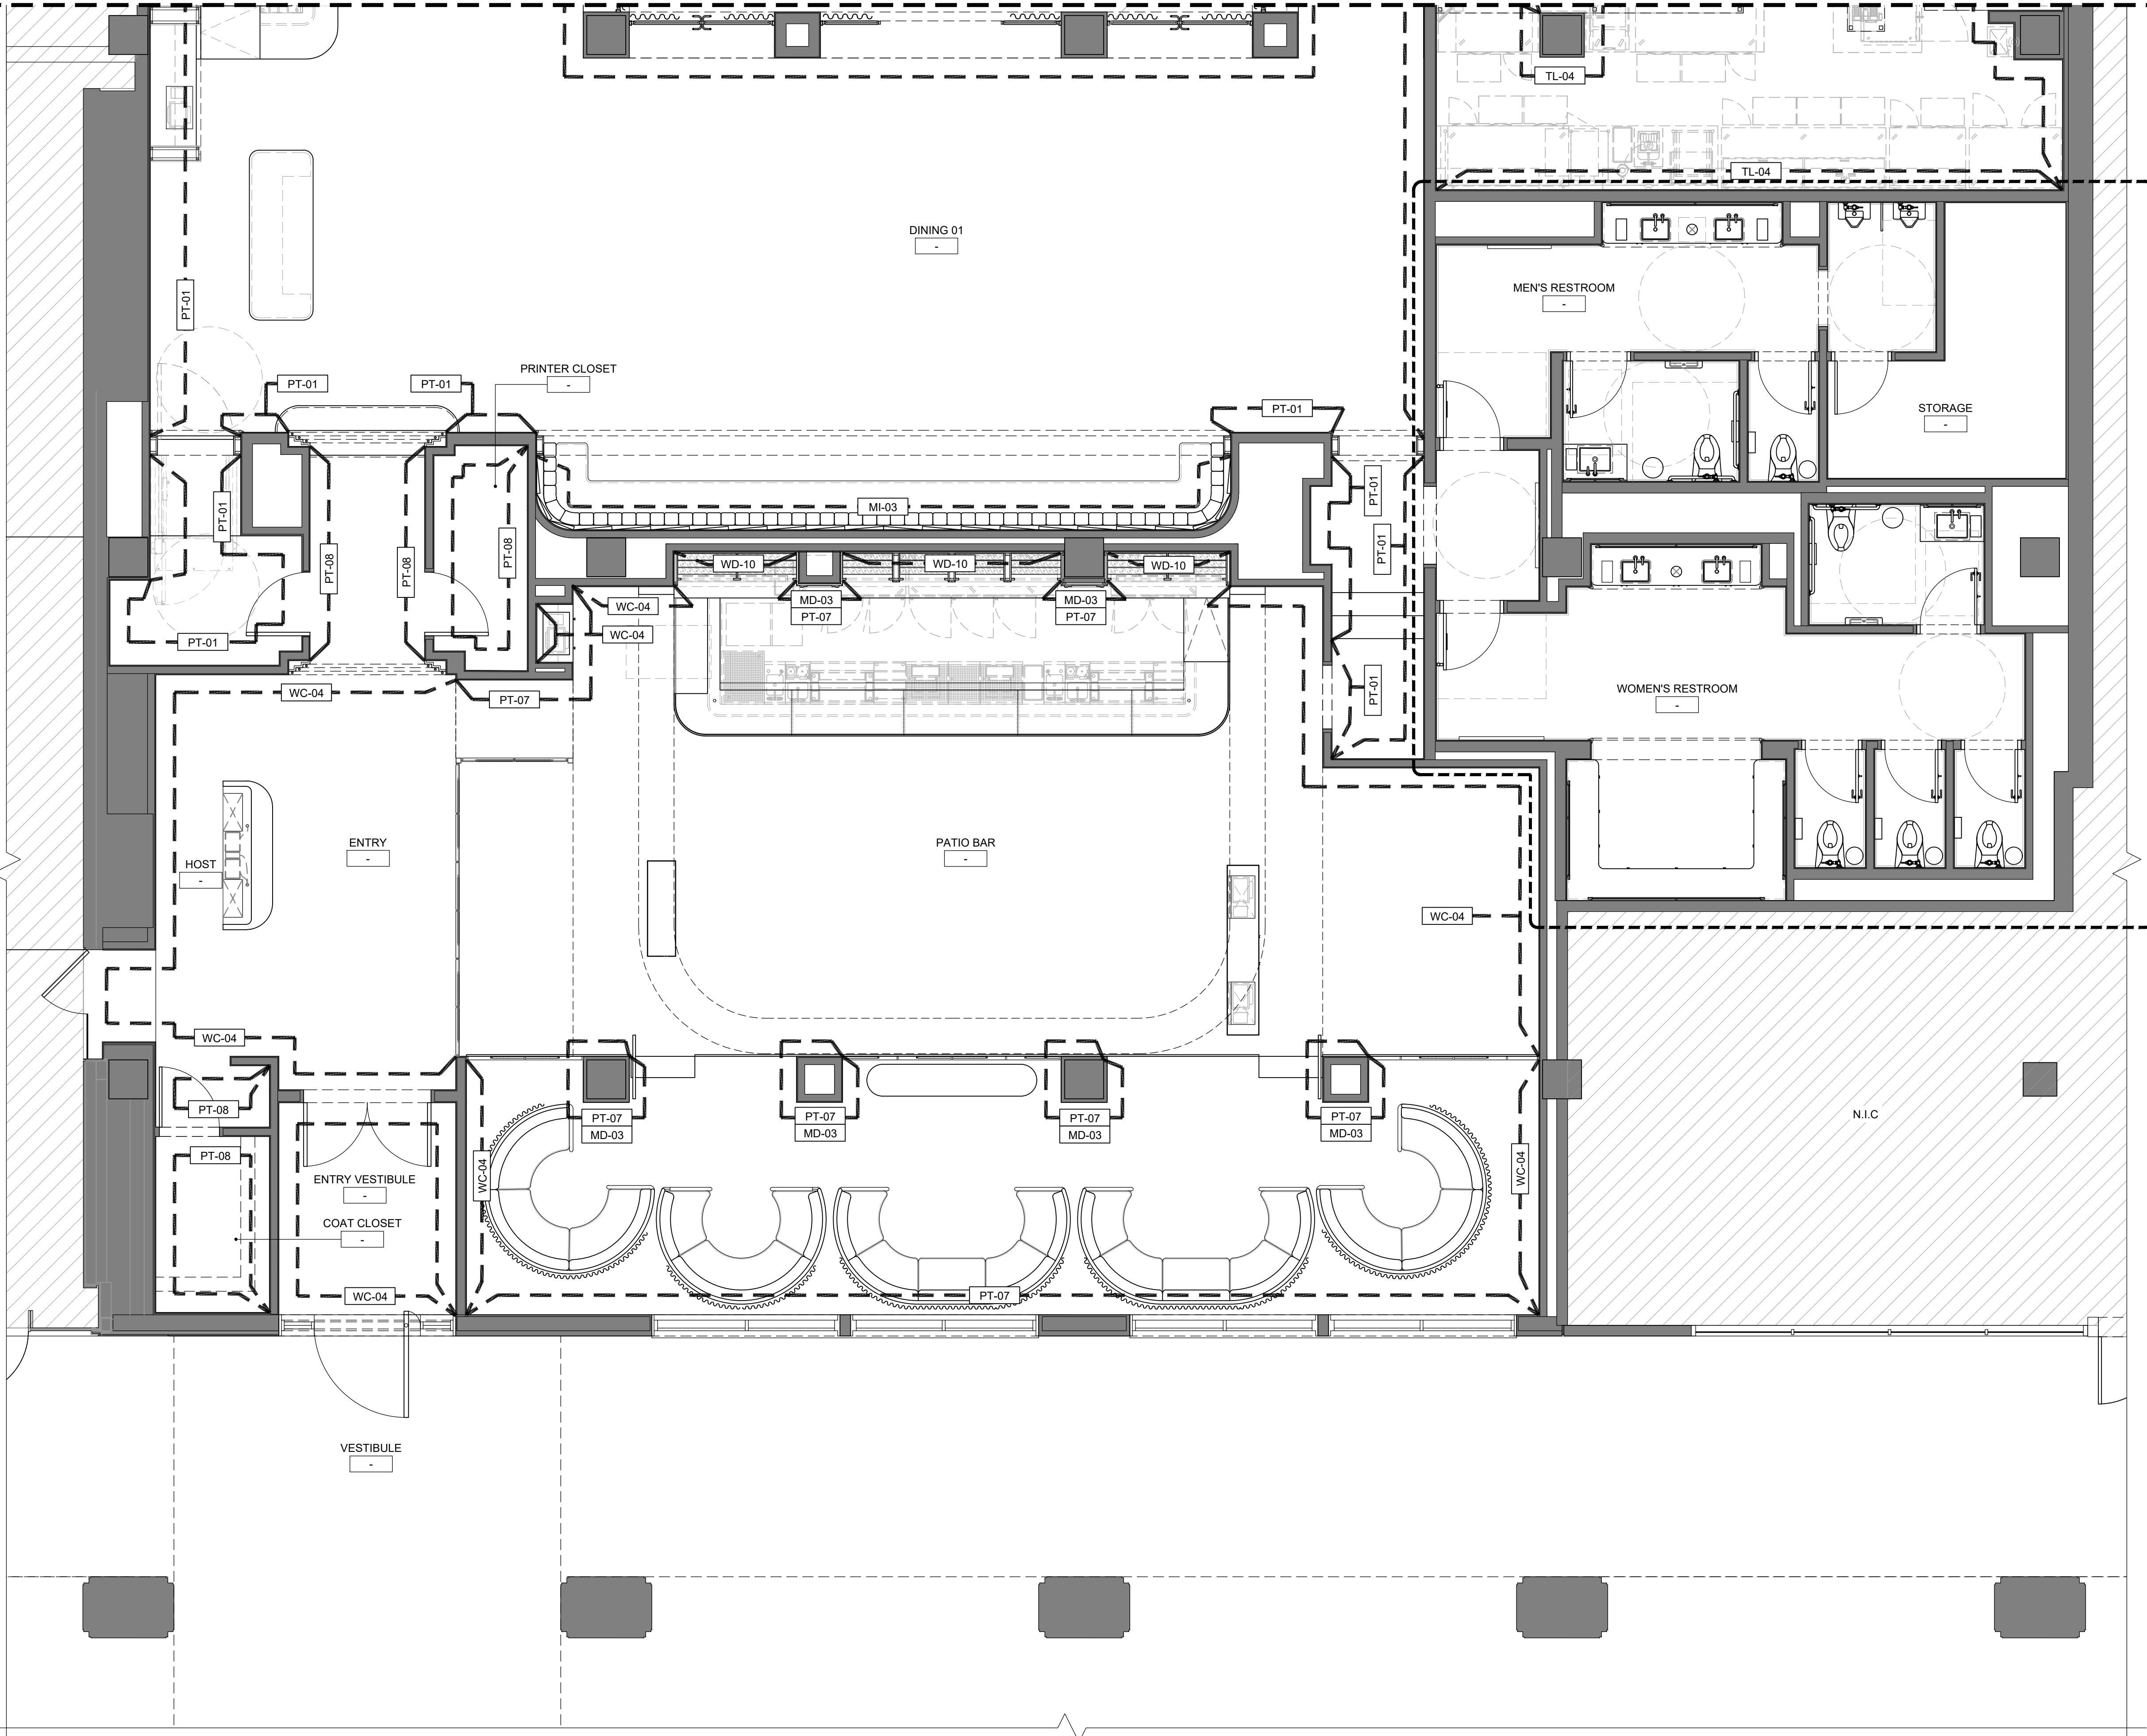

1 WALL FINISH PLAN
RESTAURANT

Scale: 1/4" = 1'-0"

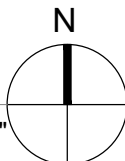

GENERAL NOTES

- A. SEE SHEET ID-1200.00 FOR ARCH FINISH SCHEDULE
B. REFER TO ELEVATIONS FOR FURTHER INFORMATION AND WALL BASE DIRECTION.

KEY NOTES

1. XXX

1
ID-702.00

FLOOR PLAN LEGEND

- EXISTING CONSTRUCTION TO REMAIN
NEW WALL PARTITION

CASS CALDER SMITH

ARCHITECTURE
INTERIORS

180 VARICK ST. #830
NEW YORK, NY 10014
212.274.1121
CASSCALDERSMITH.COM

OWNER
MAPLE HOSPITALITY GROUP

ARCHITECT
CCS ARCHITECTURE

STRUCTURAL
WRG ENGINEERING

FIRE PROTECTION & MEP
MG ENGINEERING D.P.C.

INTERIOR DESIGN
STUDIO K CREATIVE


FOOD SERVICE
GREAT LAKES CULINARY
DESIGNS

LIGHTING DESIGN
CARROLL CONSULTING

AVIT/SECURITY
GLOBAL AV GROUP

PROJECT NAME

**MAPLE & ASH
NEW YORK, NY**

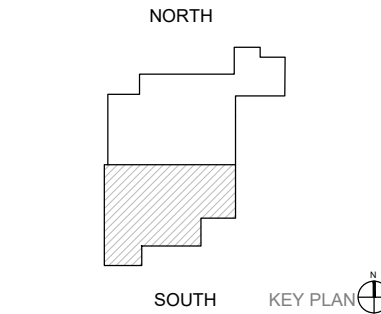

ISSUED	DESCRIPTION
10/01/2025	ISSUE FOR 50% PROGRESS SET
10/14/2025	ALT 2
10/31/2025	ISSUE FOR 100% PROGRESS SET
11/12/2025	ALT 2

SHEET TITLE

**WALL FINISH
PLAN**

FILE
BY STUDIO K
SCALE AS NOTED
SHEET

ID-510.00